
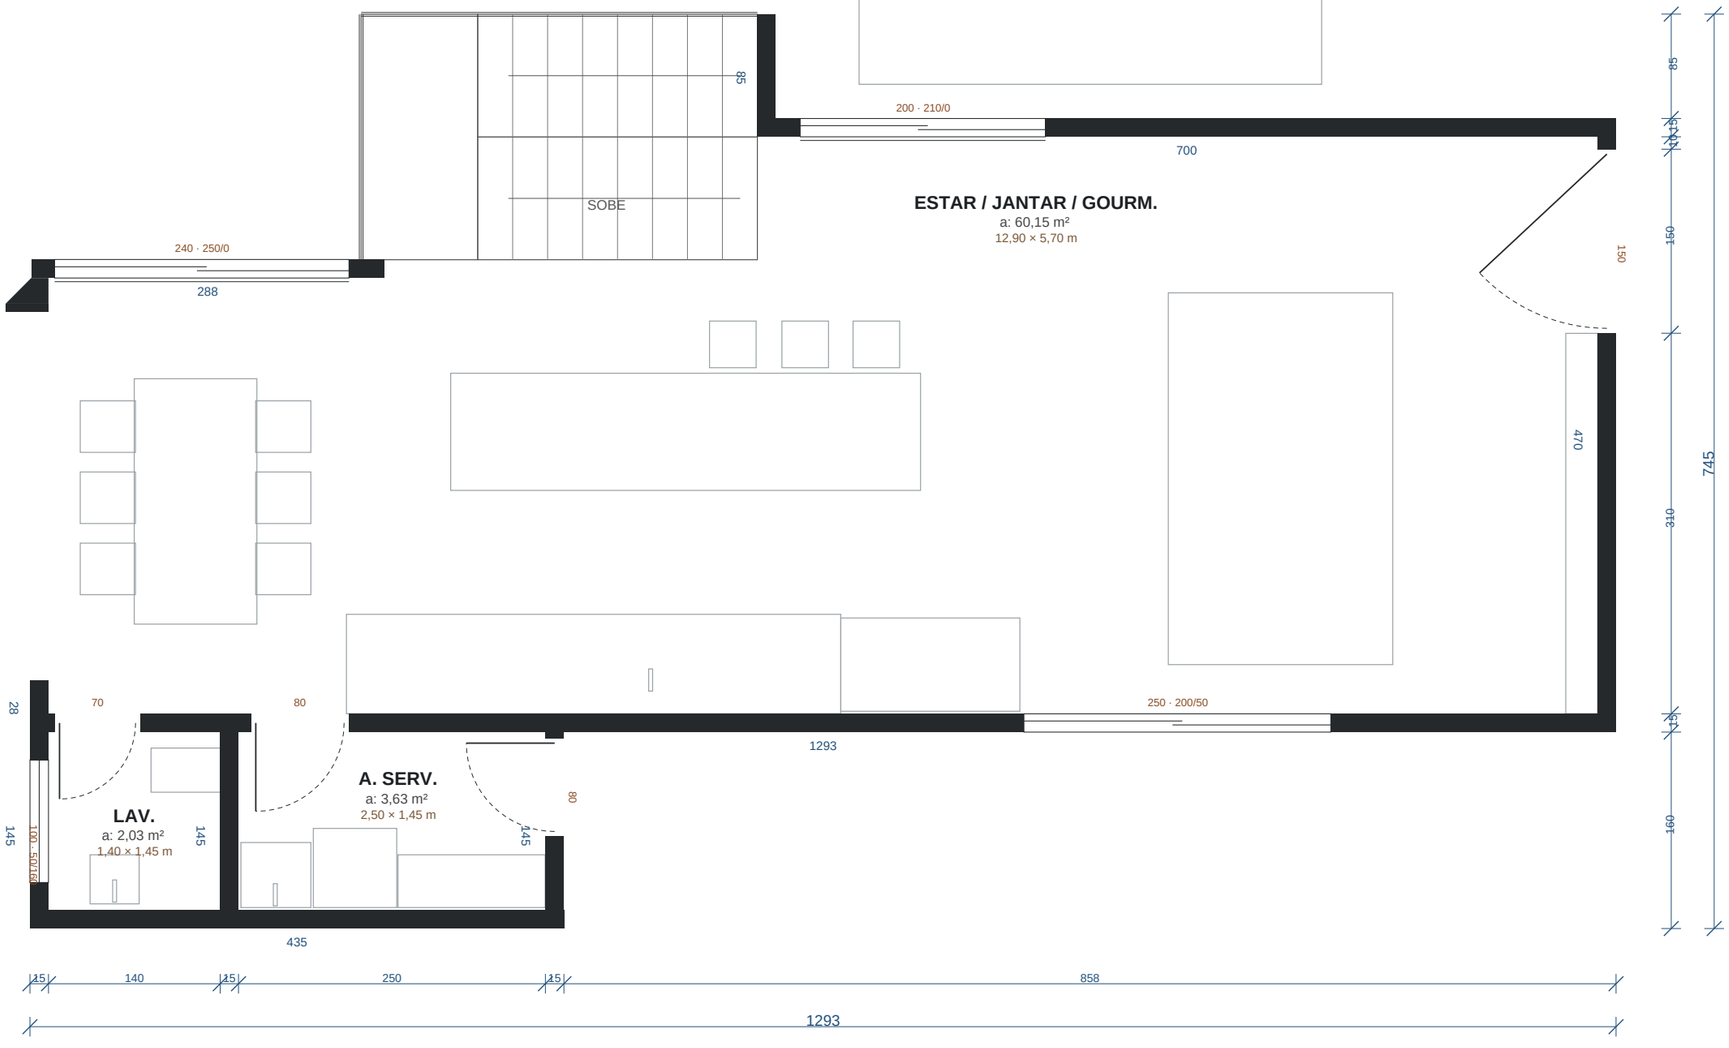


PLANTA PAV. TÉRREO

Escala 1:50 · cotas em cm · Planta original
Área útil: 65,81 m² Área construída: 72,99 m²

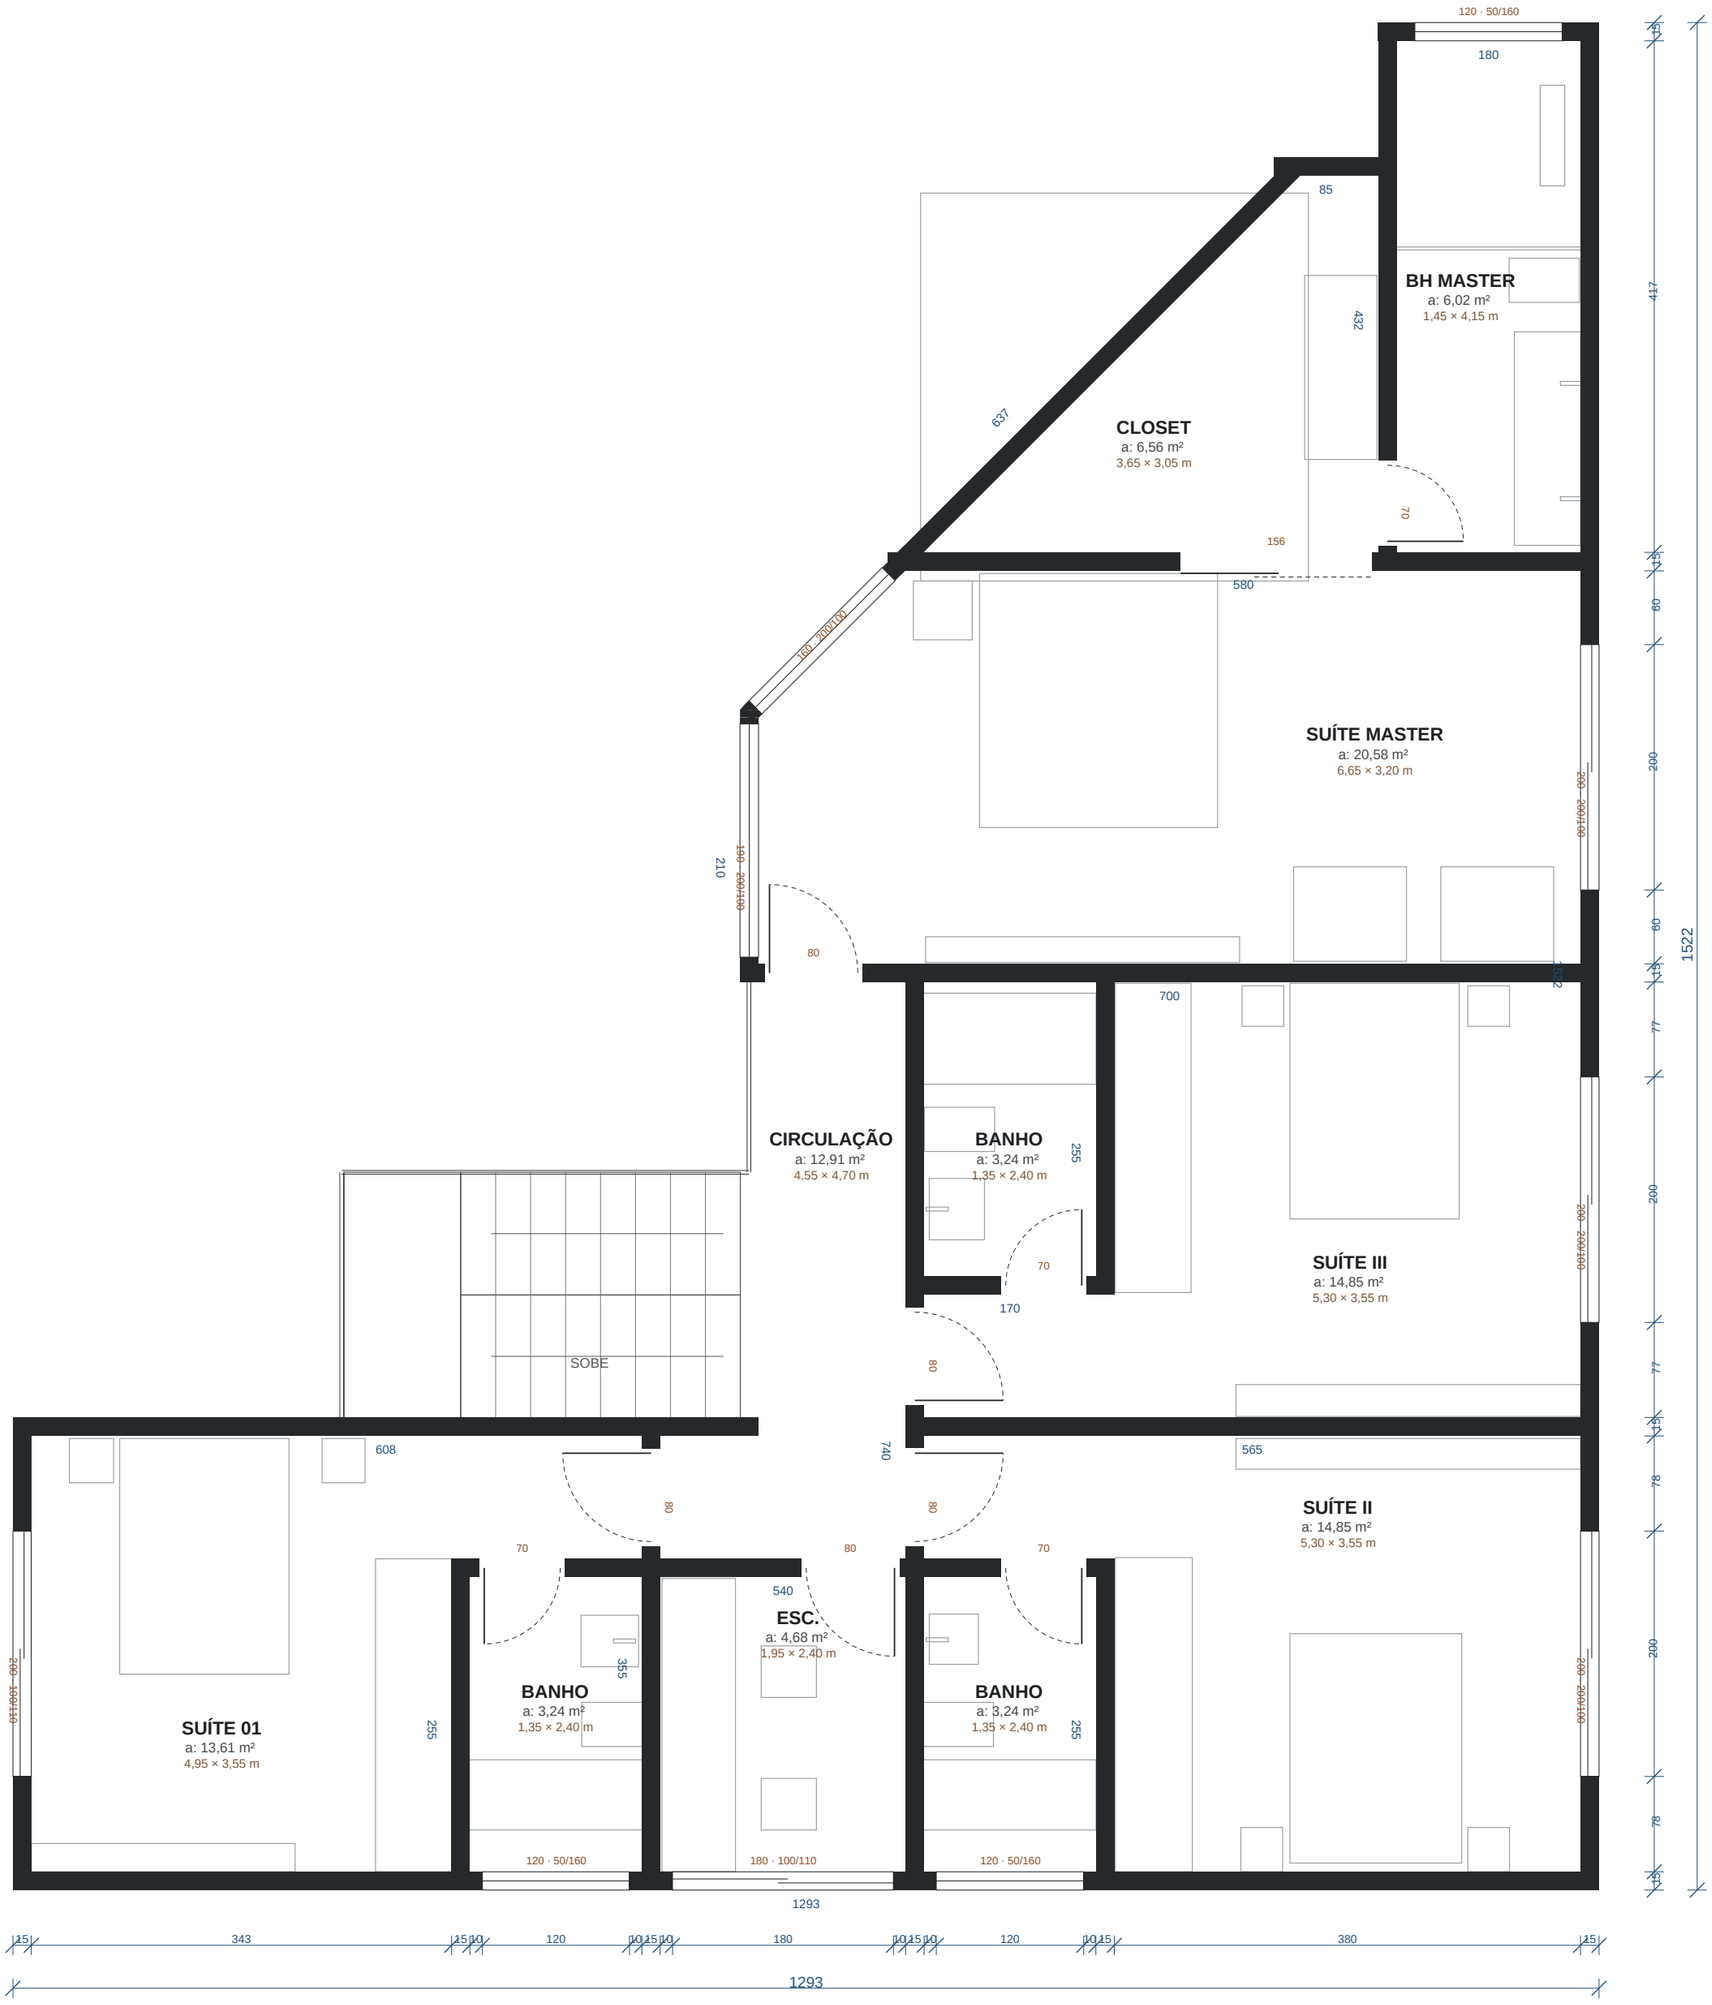

PLANTA PAV. SUPERIOR

Escala 1:50 · cotas em cm · Planta original
Área útil: 103,78 m² Área construída: 120,93 m²

Folha 2/3 · 01/11/2026

Quadro de áreas e orçamento estimado

Pavimento térreo

ESTAR / JANTAR / GOURM.	60,15 m²
GARAGEM	área aberta
LAV.	2,03 m²
A. SERV.	3,63 m²

Área útil: 65,81 m² · construída: 72,99 m²

Pavimento superior

SUÍTE 01	13,61 m²
BANHO	3,24 m²
ESC.	4,68 m²
BANHO	3,24 m²
SUÍTE II	14,85 m²
SUÍTE III	14,85 m²
BANHO	3,24 m²
SUÍTE MASTER	20,58 m²
CLOSET	6,56 m²
BH MASTER	6,02 m²
CIRCULAÇÃO	12,91 m²

Área útil: 103,78 m² · construída: 120,93 m²

Orçamento estimado (preços de referência editáveis)

Alvenaria (paredes, descontando vãos)	339,24 m²	R$ 32.228
Reboco + pintura interna (faces internas)	489,71 m²	R$ 26.934
Revestimento de fachada (faces externas)	188,76 m²	R$ 16.989
Piso porcelanato (social e circulação)	73,06 m²	R$ 12.055
Piso madeira/vinílico (quartos, closet, escritório)	75,13 m²	R$ 11.270
Piso cerâmico (áreas molhadas)	21,39 m²	R$ 2.674
Revestimento de parede em áreas molhadas (h 2,60 m)	122,98 m²	R$ 15.987
Forro/pintura de teto	169,59 m²	R$ 7.631
Contrapiso do térreo (área construída)	72,99 m²	R$ 4.380
Lajes (entrepiso + cobertura)	248,81 m²	R$ 64.691
Impermeabilização da cobertura	127,88 m²	R$ 10.870
Piso da garagem	35,33 m²	R$ 3.886
Janelas de alumínio e vidro	30,11 m²	R$ 25.593
Portas-janela	10,20 m²	R$ 9.690
Portas internas de abrir	12 un	R$ 15.600
Porta pivotante de entrada	1 un	R$ 7.500
Porta de correr	1 un	R$ 1.800
Portões	2 un	R$ 5.000

Total estimado: R$ 274.779 (R$ 1.417/m²)

Não inclui estrutura, fundação, instalações, projetos e administração da obra.